

COMMUNE
PRADES

Section **A**

2^e Feuille

Echelle: 1/2000

La mise en place des limites d'après les indications fournies au bureau est exclusivement limitée aux esquisses.


6462 T

anc. Mod. 30 Cad.
(Sept. 1970)

N° d'ordre
du document
d'arpentage **3854**

Tableau
d'assemblage [à modifier ⁽¹⁾
sans changer ⁽¹⁾

POUR COTATION VOIR PLAN CI-JOINT

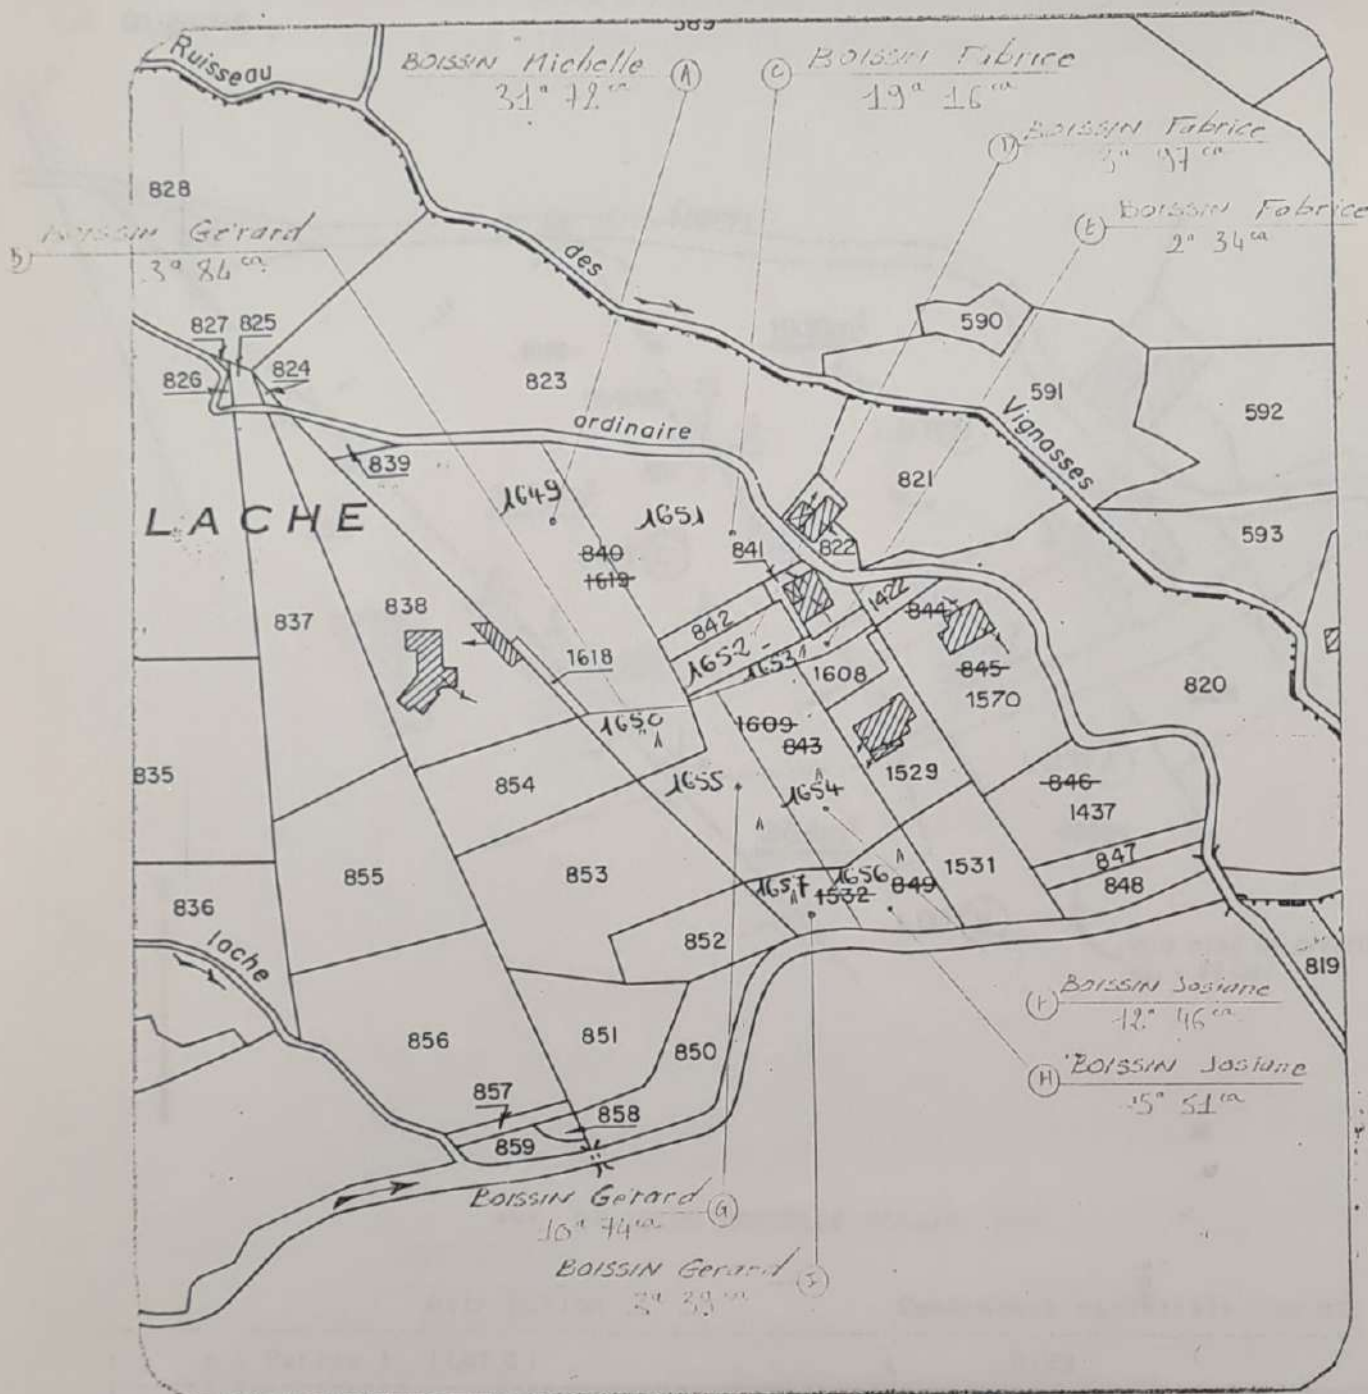

Voir la rubrique « INFORMATION DES PROPRIÉTAIRES » au dos de la chemise 6463

CERTIFICATION

(Art. 25 du décret n° 55-471 du 30 avril 1955)

Le présent document d'arpentage, certifié par les propriétaires soussignés⁽¹⁾, a été établi

A - d'après les indications qu'ils ont fournies au bureau⁽¹⁾.

B - en conformité d'un piquetage qu'ils ont effectué sur le terrain⁽¹⁾.

C - d'après un plan d'arpentage ou de bornage, dont copie ci-jointe, dressé le ... par M. HARROIS, Gervais, géomètre à AUBENAS⁽¹⁾.

Signatures

Boissin Fabrice Prades
Boissin Josiane LUSSAS
Boissin Michelle MONTELMAR
Boissin Gerard ETOILE

le 31.05.91
le 9.06.91
le 14.06.91
le 15.06.91

Document d'arpentage dressé
par M. HARROIS, Gervais
GEOMETRE-EXPERT
à AUBENAS
Date: 13-MAI-1991

Gervais HARROIS
GEOMETRE EXPERT D.P.L.G.
8, Chemin de Constantine
AUBENAS 75 93 65 57

trait du plan minute établi
par le Bureau du Cadastre⁽¹⁾,
par la personne agréée dans
les bureaux du Cadastre⁽¹⁾,
d'ordre au registre de const-
ation des droits: ...
chet de l'origine:



⁽¹⁾ Réviser les bornes in situ et les bornes n° 1 et 2 applicables dans le cas d'une esquisse (plan renvoyé par voie de mise à jour). Dans la formule B, les propriétaires peuvent avoir effectué eux-mêmes le piquetage.