

COMMUNE
de ST DIDIER. Sans AUBENAS

Section... A.....

...1... Feuille

Echelle: 1/3500...


La mise en place des limites d'après les
indications fournies au bureau est
exclusivement limitée aux esquisses.

6462 I

anc. Mod. 30 Cad.
(Sept. 1970)

N° d'ordre
du document
d'arpentage 2424

Tableau
d'assemblage à modifier (1)
sans changt (1)

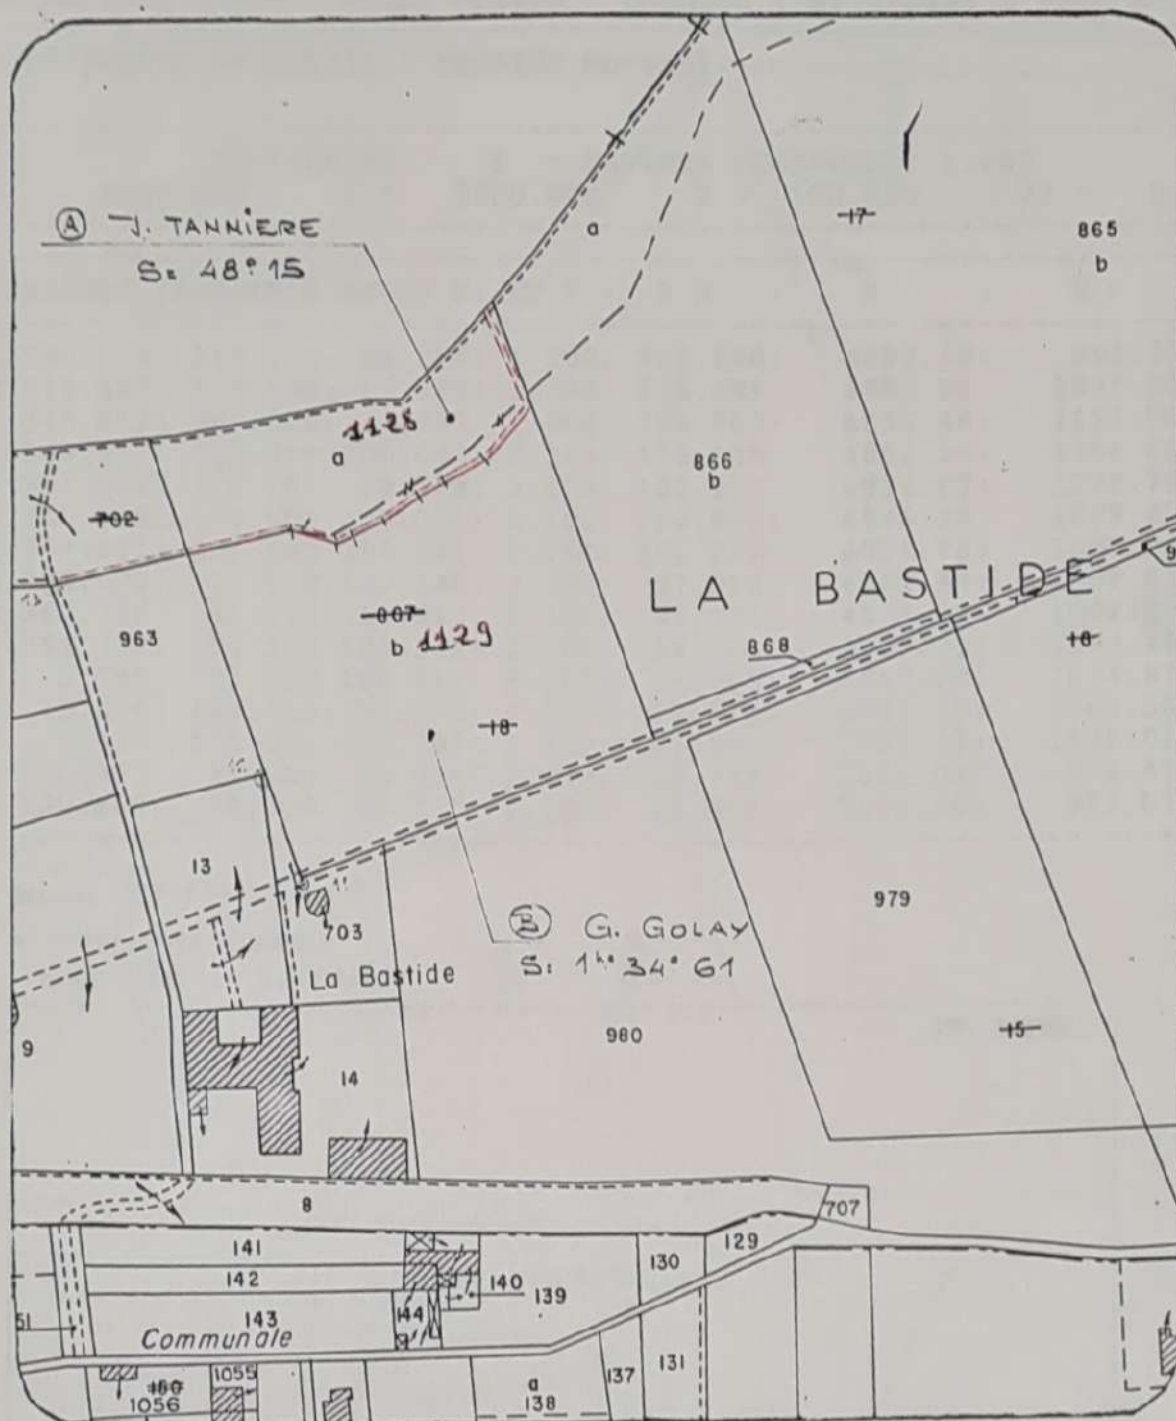

Voir la rubrique « INFORMATION DES PROPRIÉTAIRES » au dos de la chemise 6463

CERTIFICATION

(Art. 25 du décret n° 55-471 du 30 avril 1955)

Le présent document d'arpentage, certifié par les propriétaires soussignés⁽²⁾, a été établi

- A - d'après les indications qu'ils ont fournies au bureau⁽¹⁾.
B - en conformité d'un piquetage qu'ils ont effectué sur le terrain⁽¹⁾.
C - d'après un plan d'arpentage ou de bornage, dont copie ci-jointe, dressé en AVRIL 1990
par M. F. SERRET, géomètre à AUBENAS.

A ST DIDIER / AUBENAS
C. GOLAY,

le J. TANNIERE,

Document d'arpentage dressé
par M.
F. SERRET
GÉOMÈTRE - EXPERT⁽²⁾
à AUBENAS
Date: 24. Avril. 1990.

Signature:
DES GÉOMÈTRES
SERRET Fernand
Résidence Bastour
1, Bd Pasteur - B.P. 212
07204 AUBENAS CEDEX
Tel. 35.03.11

Extrait du plan minute établi
- par le Bureau du Cadastre⁽¹⁾,
- par la personne agréée dans
les bureaux du Cadastre⁽¹⁾,
N° d'ordre au registre de constatation des droits:

Cachet du Service d'origine:



(1) Rayer les mentions inutiles. La formule A n'est applicable que dans le cas d'une esquisse (plan rénové par voie de mise à jour). Dans la formule B, les propriétaires peuvent avoir effectué eux-mêmes le piquetage.

(2) Qualité de la personne agréée (géomètre-expert, inspecteur, géomètre ou technicien retraité du Cadastre, etc.).

(3) Préciser les nom et qualité du propriétaire (mandataire, avoué, représentant qualifié de l'autorité expropriante, etc.).