

Département de l'Ardèche

Commune de VALS LES BAINS

Section C - Lieudit " Rouchon "
Parcelle n°619 - Contenance cadastrale: 1ha23a16ca

Propriétaire demandeur : Mme CHABROLLE Annie

DOCUMENT DE CONSERVATION

PLAN DE BORNAGE ET PROCES VERBAL DE BORNAGE

Suite aux opérations de bornage contradictoire du 26 mai 2009



A-J-K-L Périmètre de la propriété de Mme CHABROLLE Annie bornée ce jour

Echelle 1 / 500



ORDRE DES
GEOMETRES-EXPERTS
N° d'inscription : 1992C100001

3	03.06.2009	HG	Bornage contradictoire du 26.05.2009 et pose des bornes J et K, voir PV à la suite
2	06.04.2009	ND	Complément de levé du 24.03.2009
1	30.01.2007	HG	Opérations de terrain et levé du 08.05.2005
Version	Date	Dessiné par	Observations

Géomètres-Experts - Ingénierie - Bureau d'Etudes d'Aménagement

AUBENAS

siège

Avenue Jean Monnet - Quartier Pialon - BP 212 - 07204 AUBENAS Cedex
Tél 04 75 35 69 70 - Fax 04 75 93 33 48 - E-mail : aubenas@geo-siapp.com

VALLON PONT D'ARC

bureaux
secondaires


Rue des Ecoles - 07150 VALLON PONT D'ARC

Tél 04 75 88 42 30 - Fax 04 75 88 16 94 - E-mail : vallon@geo-siapp.com

GUILHERAND GRANGES

Immeuble Le Mercure - 370 Rue Montgolfier - 07500 GUILHERAND GRANGES

GEO-SIAPP S.A.

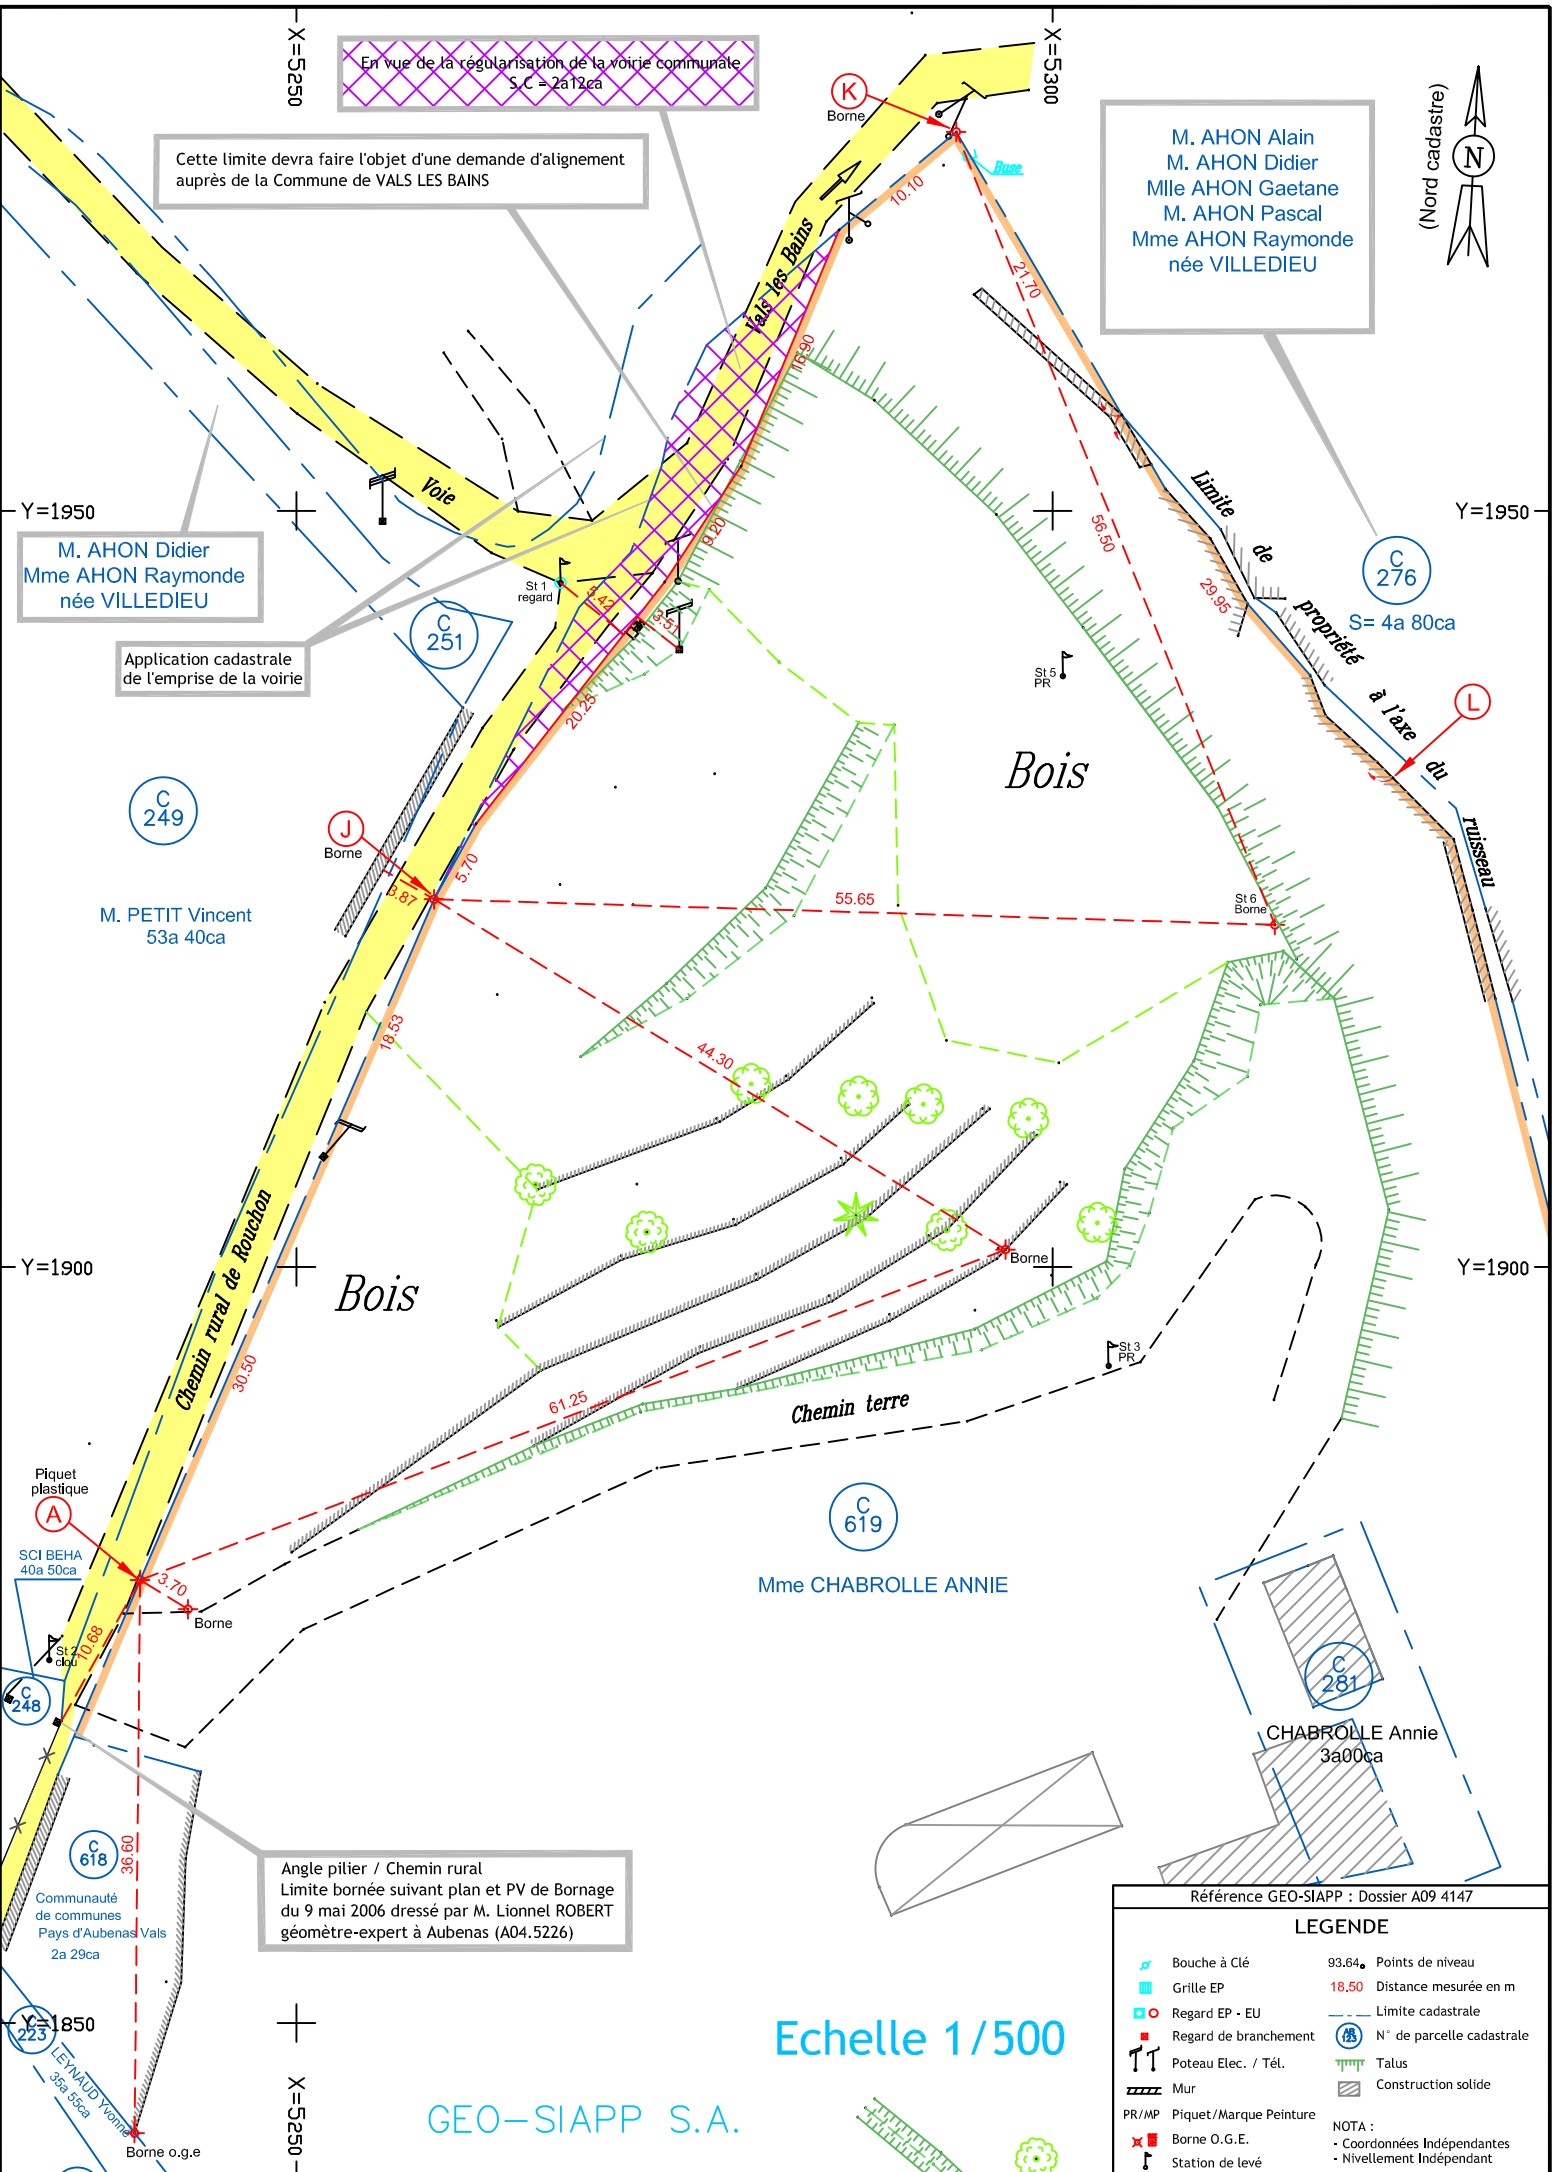

PROCÈS-VERBAL DE BORNAGE

Les opérations ont été conduites à la demande de Mme CHABROLLE Annie.

Les propriétaires ont été convoqués par lettre simple du 15 mai 2009.

Les propriétaires soussignés approuvent le présent plan valant procès-verbal de bornage, fixant les limites de leurs propriétés respectives telles qu'ils les ont définies avec le concours du Géomètre-Expert soussigné et acceptées sans réserve. Les dites limites sont matérialisées et repérées comme indiqué sur le plan pour servir leur reconnaissance ou rétablissement éventuel.

Les soussignés affirment qu'il n'existe, à ce jour, à leur connaissance, pas d'autre borne ou signe de délimitation concernant les limites présentes définies. S'il s'en découvrait, par la suite, les parties concernées les considéreraient comme nuls.

Les soussignés déclarent, sous leur entière responsabilité, être les propriétaires des terrains bornés ou délimités par le présent acte ou avoir dûment reçu pouvoir de l'approuver de tous les ayants-droit qu'ils représentent.

Une fois signé, un exemplaire de ce document ou une copie certifiée conforme sera adressée gratuitement aux parties par le Géomètre-Expert.

Date et signature des propriétaires, précédée de la mention "Lu et approuvé"

Mme CHABROLLE Annie

Lu et approuvé
Chabrolle
M. AHON Didier
Lu et approuvé
Ahon

MMme MOULIN Franck

"Lu et approuvé"
Moulin

M. AHON Pascal

Lu et approuvé
Ahon

Mlle AHON Gaetane

Lu et approuvé
Ahon

Mme AHON Raymonde
née VILLEDIEU

Lu et approuvé
Ahon

M. AHON Alain

Tuteur légal M. AHON Pascal

Lu et approuvé
Ahon

M. PETIT Vincent

Lu et approuvé
Petit

Cne de VALS LES BAINS


représentée lors des opérations de terrain
par M. LACROTTE Robert

Lu et approuvé
Lacrotte

GEO-SIAPP
Le Géomètre-Expert
M. Lionnel ROBERT

Géo-Siapp s.a.
Lionnel ROBERT
Géomètre-Expert D.P.L.G.
Inscrit sous le n° 5141
BP 212
07204 AUBENAS Cedex

ORDRE DES
GEOMETRES-EXPERTS
N° d'inscription : 1992C100001

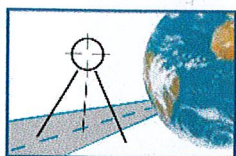

GEO-SIAPP S.A.

Géomètres-Experts - Ingénierie - Bureau d'Etudes d'Aménagement

AUBENAS

siège

Avenue Jean Monnet - Quartier Pialon - BP 212 - 07204 AUBENAS Cedex
Tél 04 75 35 69 70 - Fax 04 75 93 33 48 - E-mail : aubenas@geo-siapp.com

VALLON PONT D'ARC

bureaux
secondaires

Rue des Ecoles - 07150 VALLON PONT D'ARC

Tél 04 75 88 42 30 - Fax 04 75 88 16 94 - E-mail : vallon@geo-siapp.com

GUILHERAND GRANGES

Immeuble Le Mercure - 370 Rue Montgolfier - 07500 GUILHERAND GRANGES
Tél 04 75 81 32 33 - Fax 04 75 81 32 34 - E-mail : guilherand@geo-siapp.com