

Cession MACCHI et GUEDJ à FILLIAT

PLAN D'ARPENTAGE ET DE DIVISION

Cession MACCHI à FILLIAT
Partie du n° 47 Surface acquise par Monsieur FILLIAT Cédric Sb= 01a86ca

Cession GUEDJ à FILLIAT
Partie du n°48 Surface acquise par Monsieur FILLIAT Cédric Sc= 02a17ca

	Mme MACCHI Anaïs	M. GUEDJ Daniel	M. GUEDJ Denise née FOUQUE	M. FILLIAT Cédric
Date et signature	02.04.19 	26/03/2019 	20/03/2019 	

Echelle 1/500

1	04.03.2019	HD	Opérations de levé du 19.04.2016 et bornage du 20.06.2016
Version	Date	Dessiné par	Observations




Géomètres-Experts - Bureau d'Etudes et maîtrise d'œuvre - Environnement - Urbanisme

AUBENAS siège
2 Avenue Jean Monnet - Quartier Pialon - BP 90212 - 07204 AUBENAS Cedex
Tél 04 75 35 69 70 - Fax 04 75 93 33 48 - E-mail : aubenas@geo-siapp.com

VALLON PONT D'ARC bureaux
Rue Lorion Blachère - 07150 VALLON PONT D'ARC
Tél 04 75 88 42 30 - Fax 04 75 88 16 94 - E-mail : vallon@geo-siapp.com

GUILHERAND GRANGES secondaires
Immeuble Le Mercure - 370 Rue Montgolfier - 07500 GUILHERAND GRANGES
Tél 04 75 81 32 33 - Fax 04 75 81 32 34 - E-mail : guilherand@geo-siapp.com

PIERRELATTE
4 rue André Le Nôtre - 26700 PIERRELATTE
Tél 04 75 96 84 81 - Fax 04 75 96 40 49 - E-mail : pierrelatte@geo-siapp.com

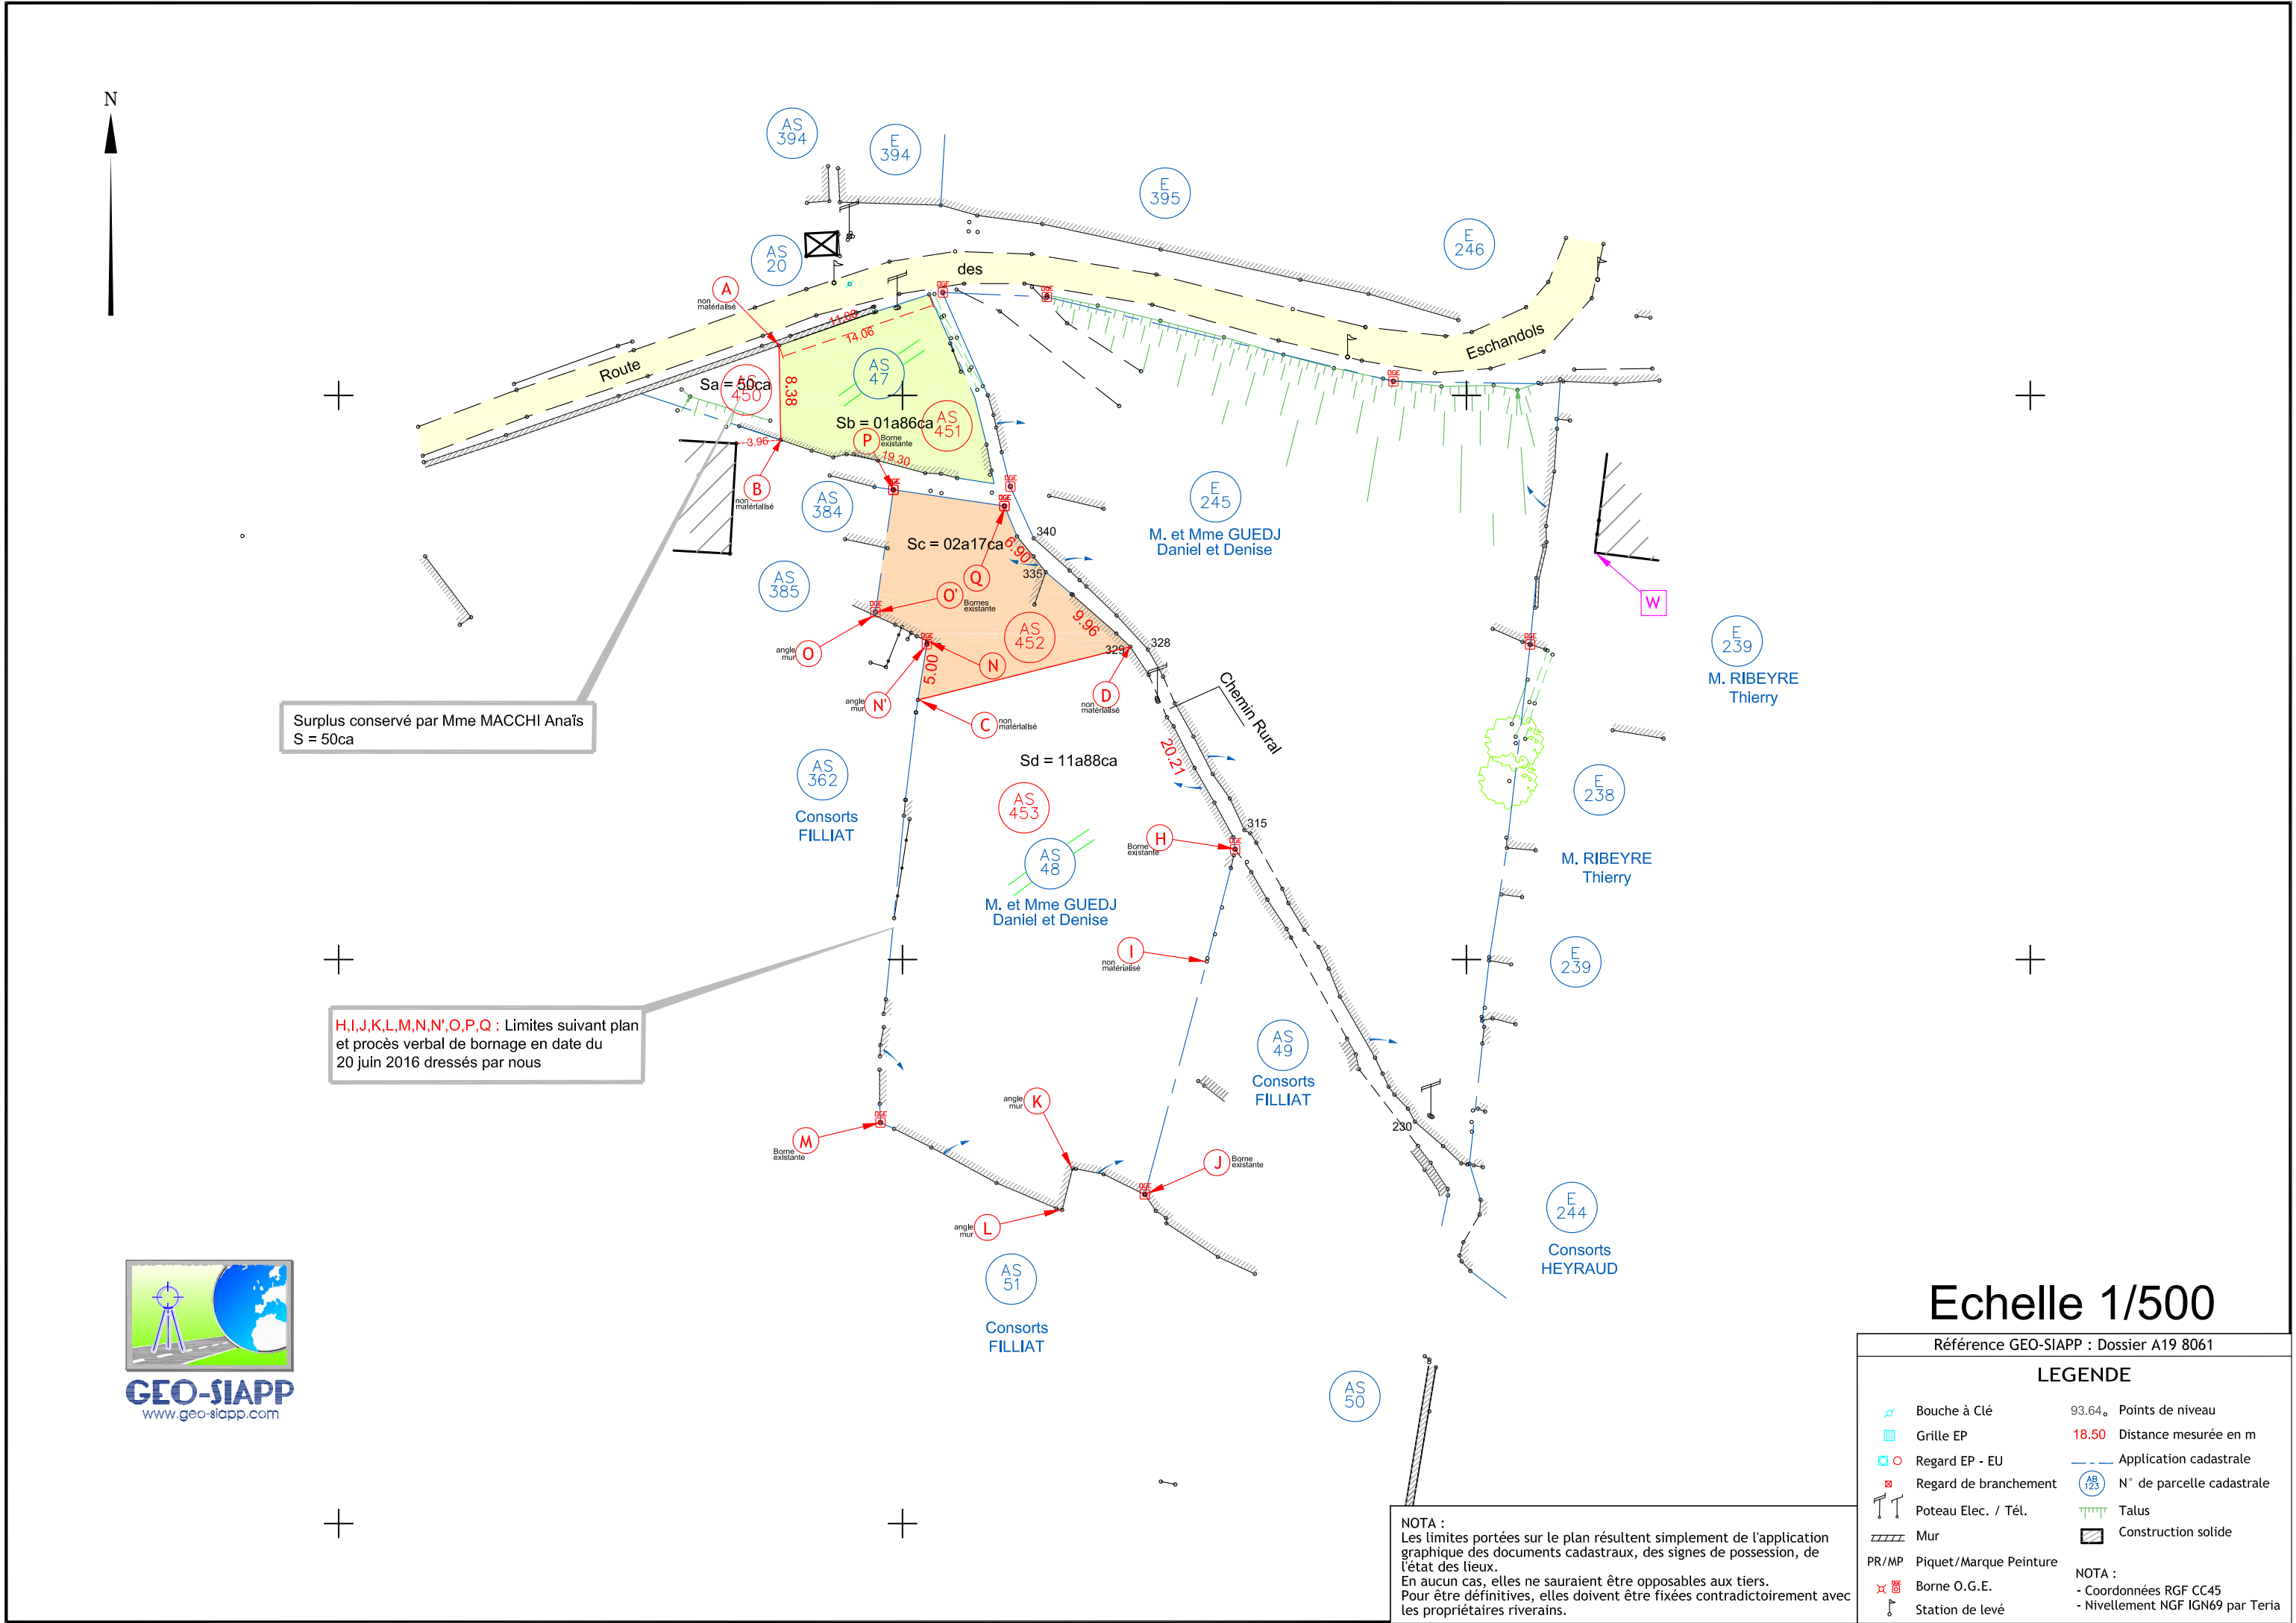

Echelle 1/500

Référence GEO-SIAPP : Dossier A19 8061			
LEGENDE			
	Bouche à Clé		93.64. Points de niveau
	Grille EP		18.50 Distance mesurée en m
	Regard EP - EU		Application cadastrale
	Regard de branchement		N° de parcelle cadastrale
	Poteau Elec. / Tél.		Talus
	Mur		Construction solide
	PR/MP Piquet/ Marque Peinture	NOTA :	
	Borne O.G.E.	- Coordonnées RGF CC45	
	Station de levé	- Nivellement NGF IGN69 par Teria	