

COMMUNE
Saint Privat.....
Section... *AL*..
.....^e Feuille
Echelle: 1/1000...


6462 T

anc. Mod. 30 Cad.
(Sept. 1970)

N° d'ordre
du document
d'arpentage *608.A*

Tableau
d'assemblage à modifier ⁽¹⁾
sans changt ⁽¹⁾

*Pour cotation
Voir plan
annexe.*

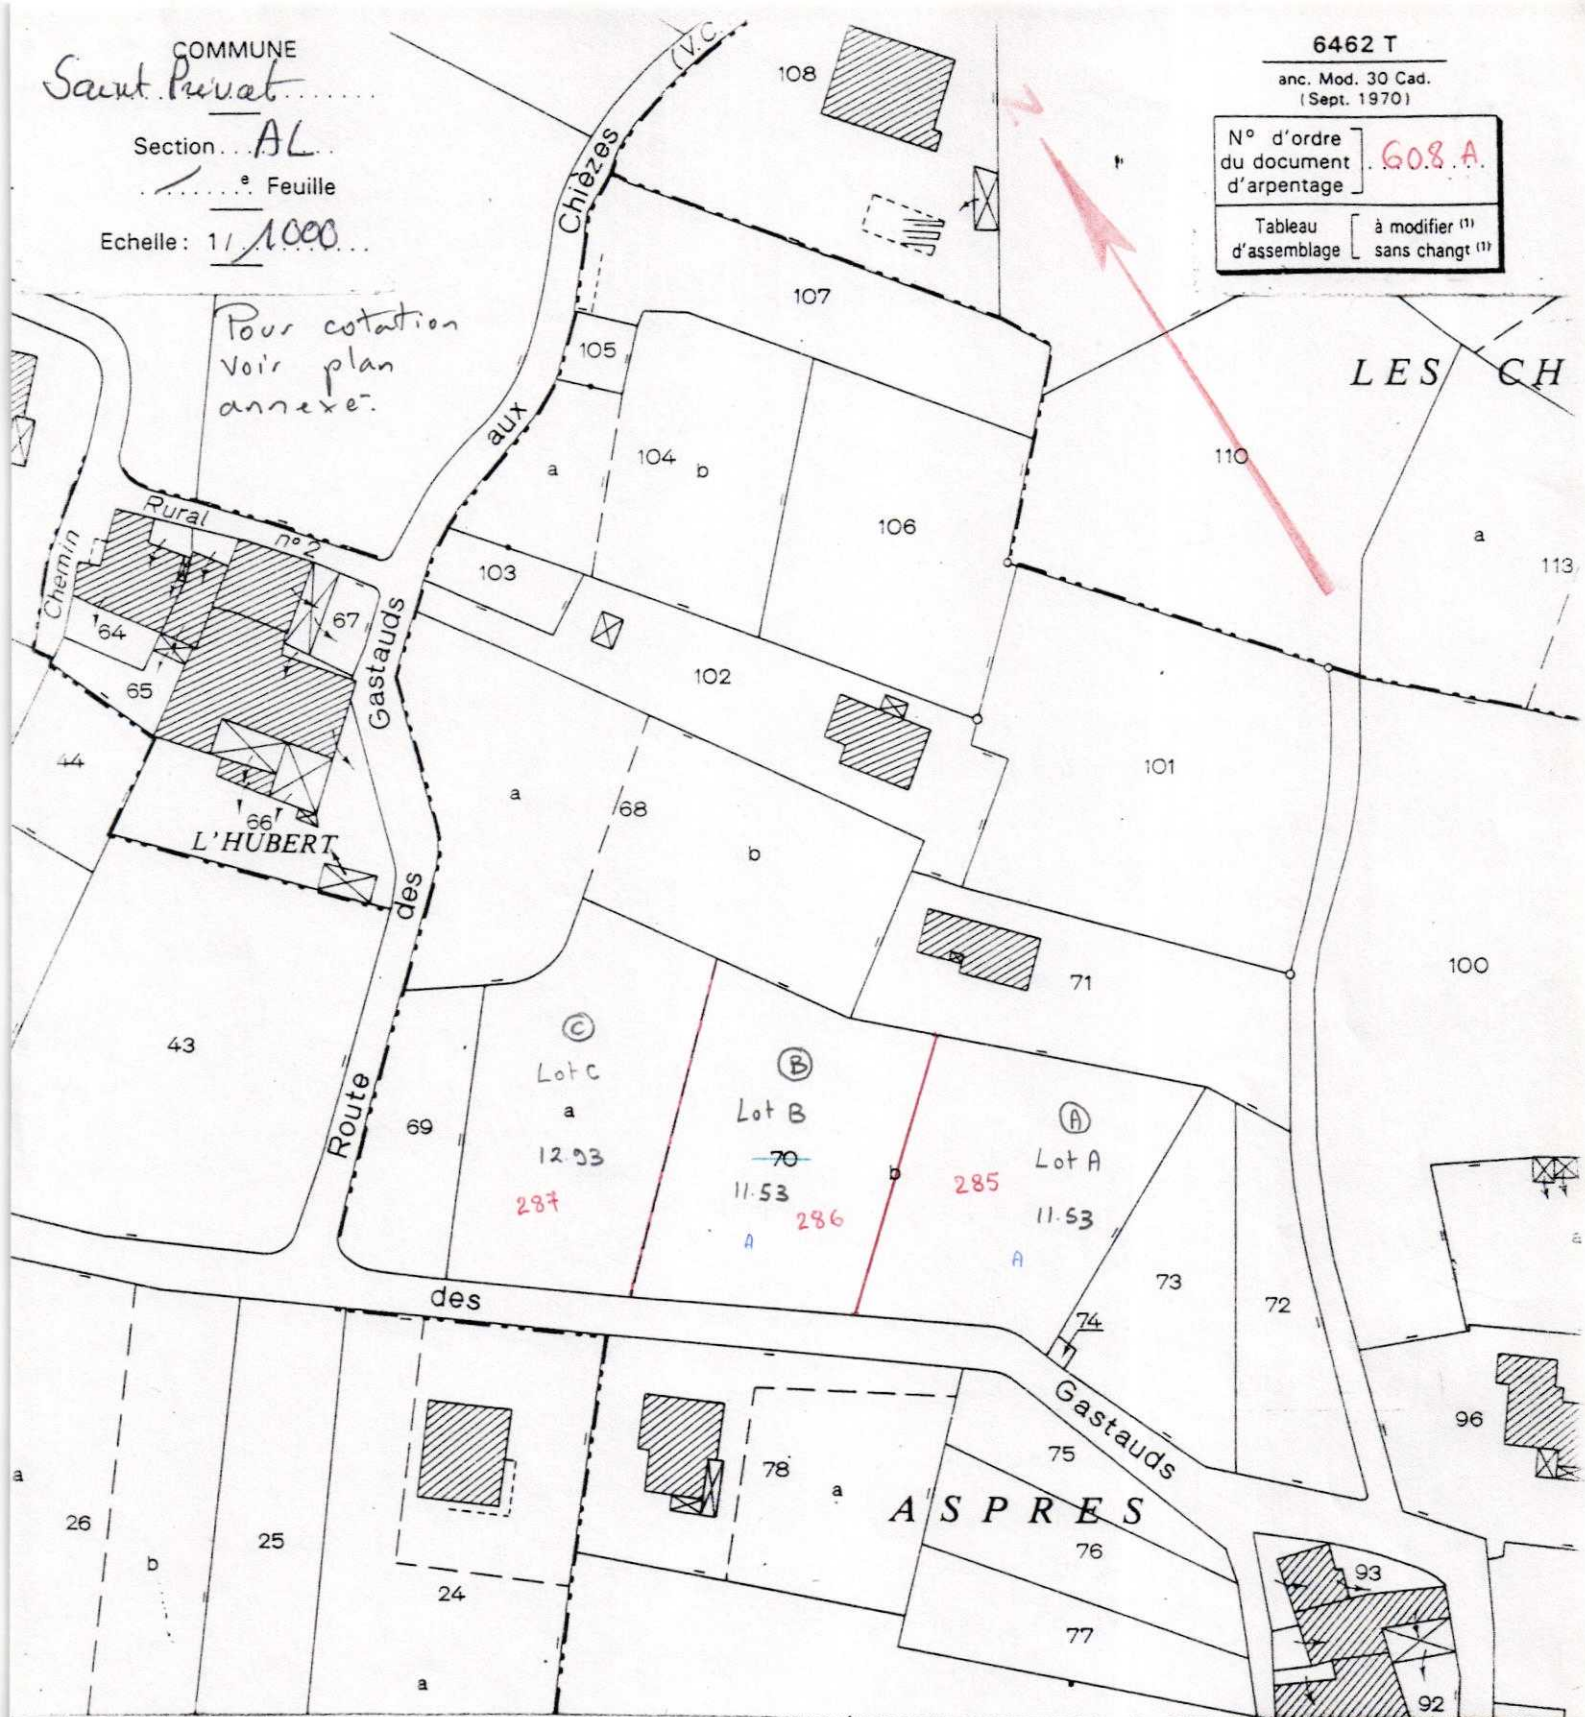

Extrait du plan minute établi
- par le Bureau du Cadastre⁽¹⁾.
- par la personne agréée dans
les bureaux du Cadastre⁽¹⁾.
N° d'ordre au registre de cons-
tation des droits: *1413*.
Cachet du Service d'origine:

Voir la rubrique « INFORMATION DES PROPRIÉTAIRES » au dos de la chemise 6463

CERTIFICATION

(Art. 25 du décret n° 55-471 du 30 avril 1955)

Le présent document d'arpentage, certifié par les propriétaires soussignés⁽³⁾, a été établi

A - d'après les indications qu'ils ont fournies au bureau⁽¹⁾.

B - en conformité d'un piquetage qu'ils ont effectué sur le terrain⁽¹⁾.

C - d'après un plan d'arpentage ou de bornage, dont copie ci-jointe, dressé le

par M, géomètre à

A *Saint Privat*, le *01.12.97*

T. COSTARGENT

Document d'arpentage dressé
par M. *HARROIS*.....
Géomètre.....
Expert.....⁽²⁾.
à *Aubenas*.....
Date: *14.10.97*.....
Signature:

Gervais HARROIS
⁽¹⁾ GEOMETRE EXPERT D.P.L.G.
8, Chemin de Constantine
07200 AUBENAS 75 93 65 57.

6462 T

(1) Rayer les mentions inutiles. La formule A n'est applicable que dans le cas d'une esquisse (plan rénové par voie de mise à jour). Dans la formule B, les propriétaires peuvent avoir effectué eux-mêmes le piquetage.

(2) Qualité de la personne agréée (géomètre-expert, inspecteur, géomètre ou technicien retraité du Cadastre, etc.).

(3) Préciser les nom et qualité du signataire s'il est différent du propriétaire (mandataire, avocat, représentant qualifié de l'autorité expropriante, etc.).